


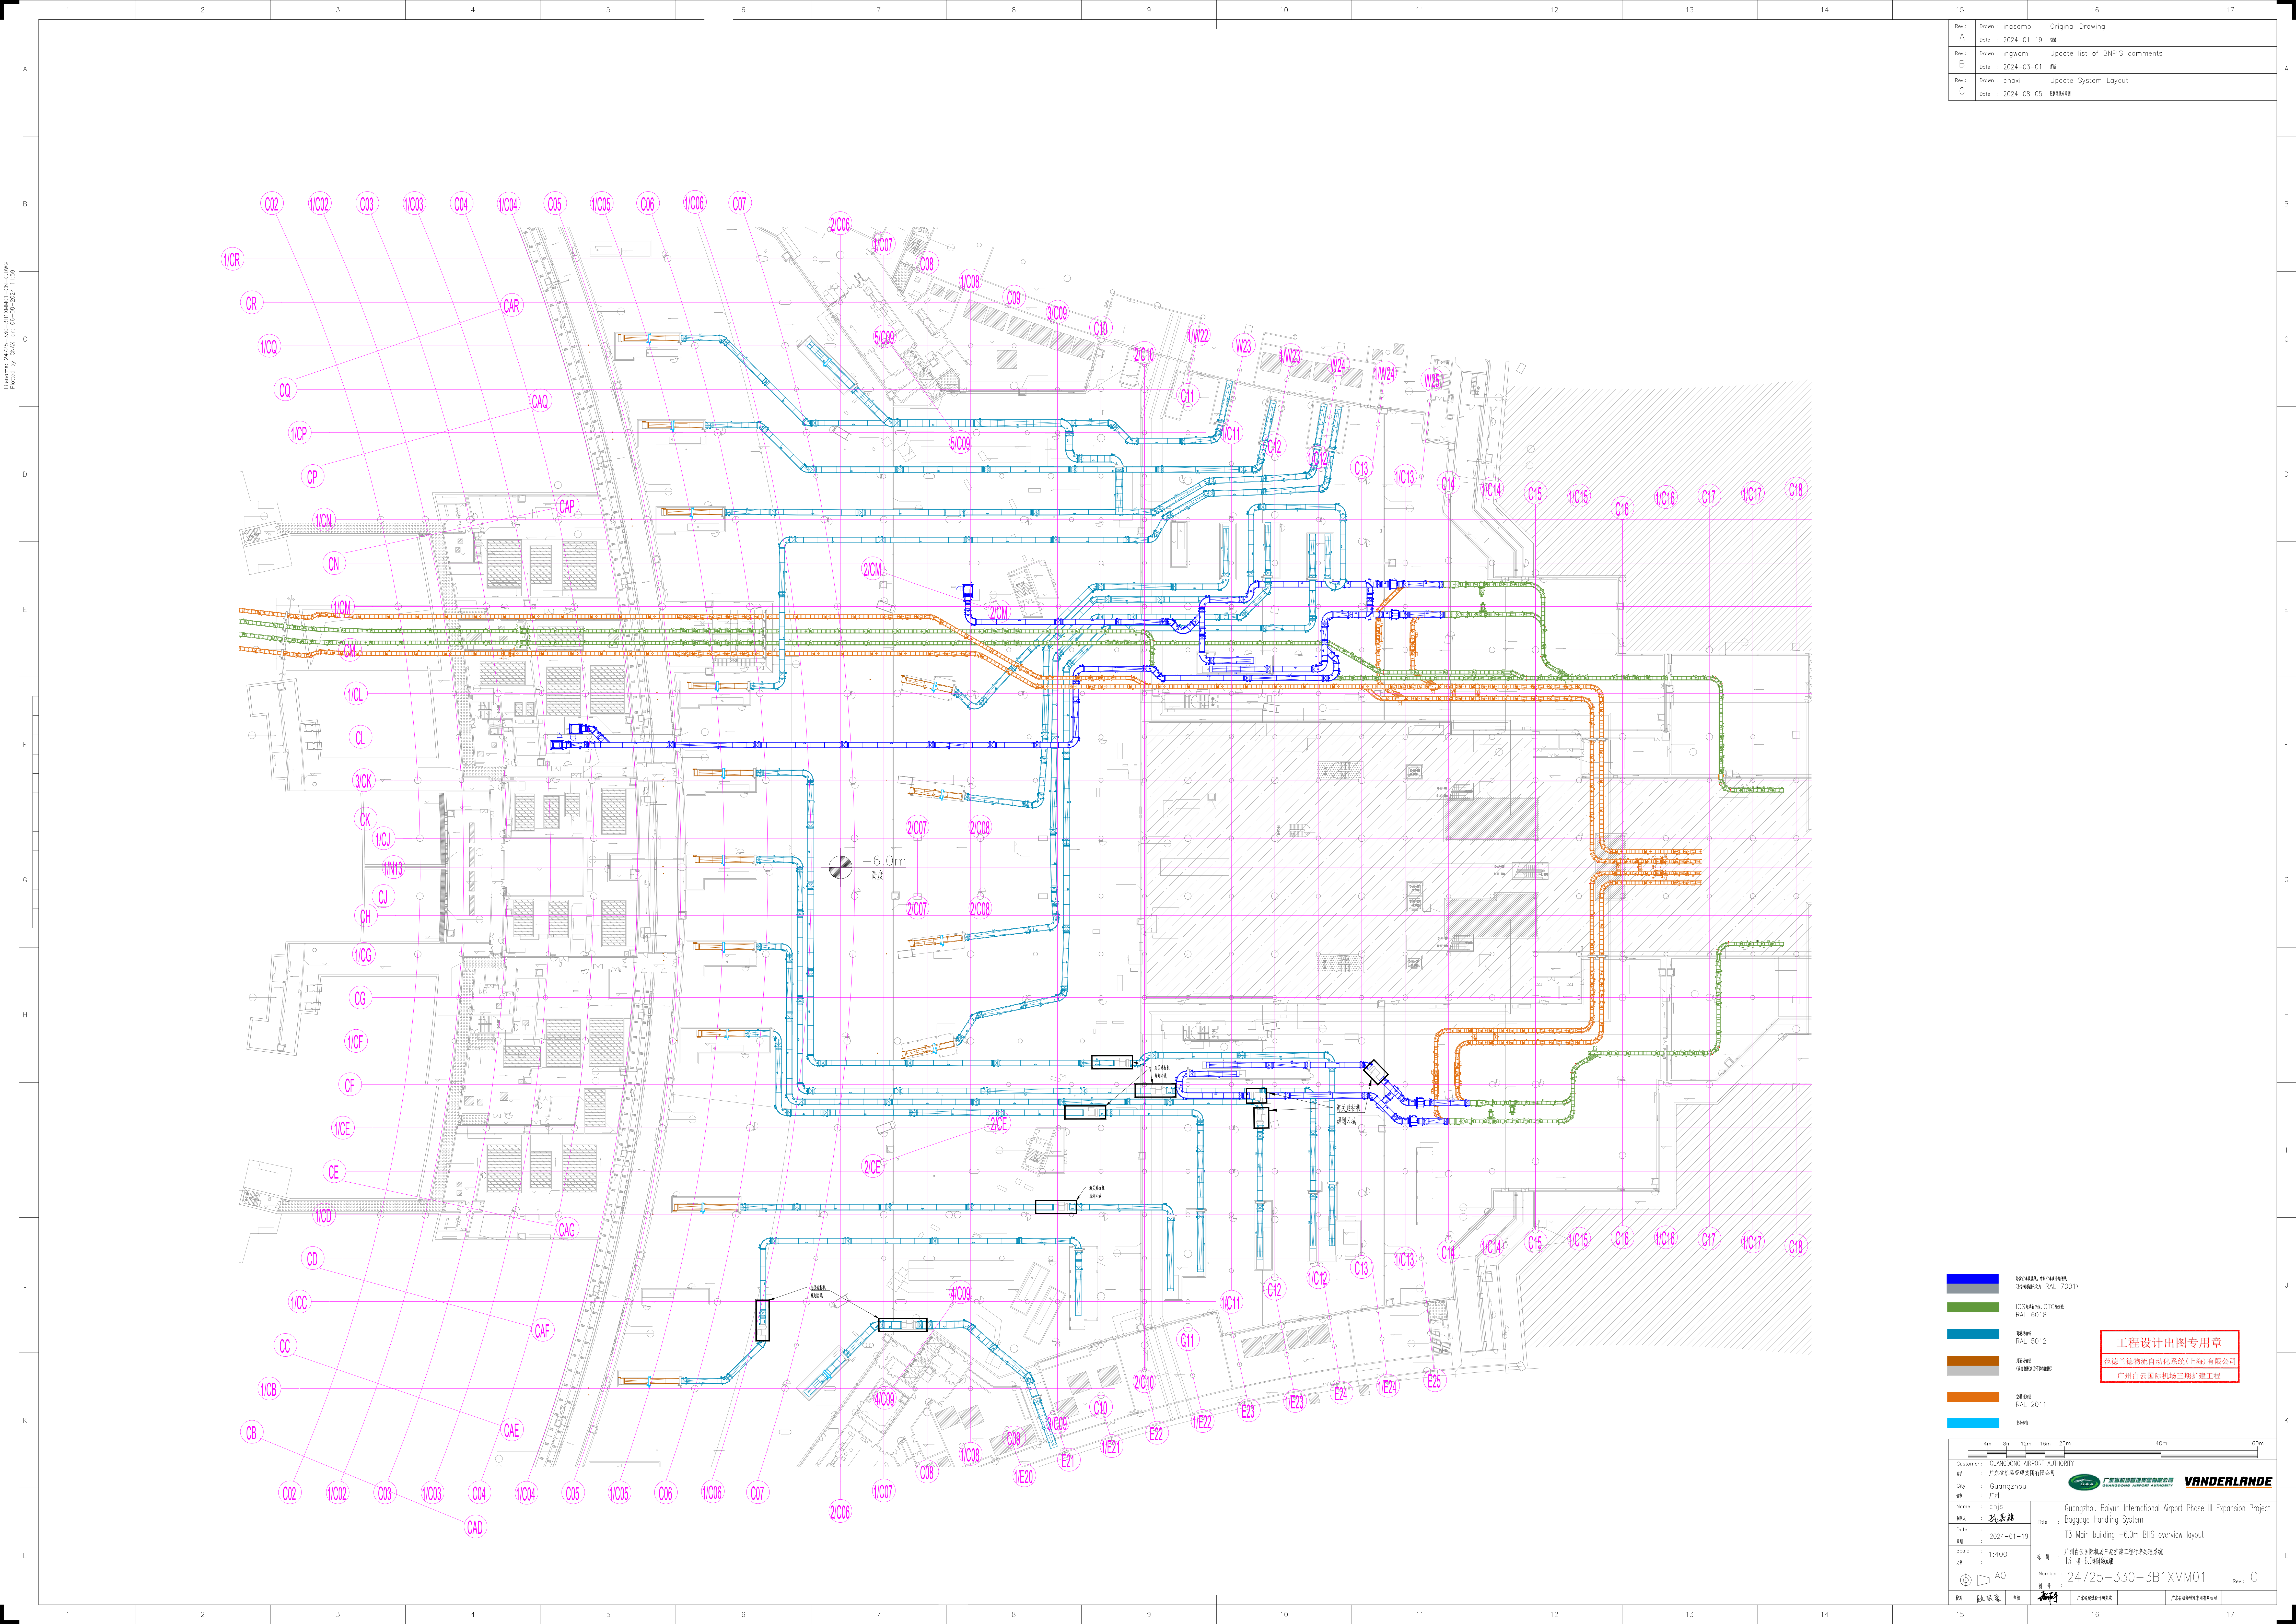

Rev:	Draw:	Original Drawing
A	date: 2024-01-19	00
Rev:	Draw:	Update list of BNP's comments
B	date: 2024-03-01	01
Rev:	Draw:	Update System Layout
C	date: 2024-08-05	02

蓝色涂层, 特制环氧富锌底漆
(符合ISO 12944-5:2018 RAL 7001)

绿色涂层, GTC涂层
(符合ISO 12944-5:2018 RAL 5018)

蓝色涂层
(符合ISO 12944-5:2018 RAL 5012)

棕色涂层
(符合ISO 12944-5:2018 RAL 2011)

黄色涂层
(符合ISO 12944-5:2018 RAL 2011)

工程设计出图专用章

范德兰德物流自动化系统(上海)有限公司
广州白云国际机场三期扩建工程

4m 8m 12m 16m 20m 40m 60m	
Customer: GUANGDONG AIRPORT AUTHORITY	广东机场集团有限公司
City: Guangzhou	广州
Name: cnjs	Guangzhou Baiyun International Airport Phase III Expansion Project
Version: 2024-01-19	Baggage Handling System
Scale: 1:400	T3 Main building -6.0m BHS overview layout
Number: 24725-330-3B1XMM01	广州白云国际机场三期扩建工程行李处理系统
Rev: C	广东机场集团有限公司