


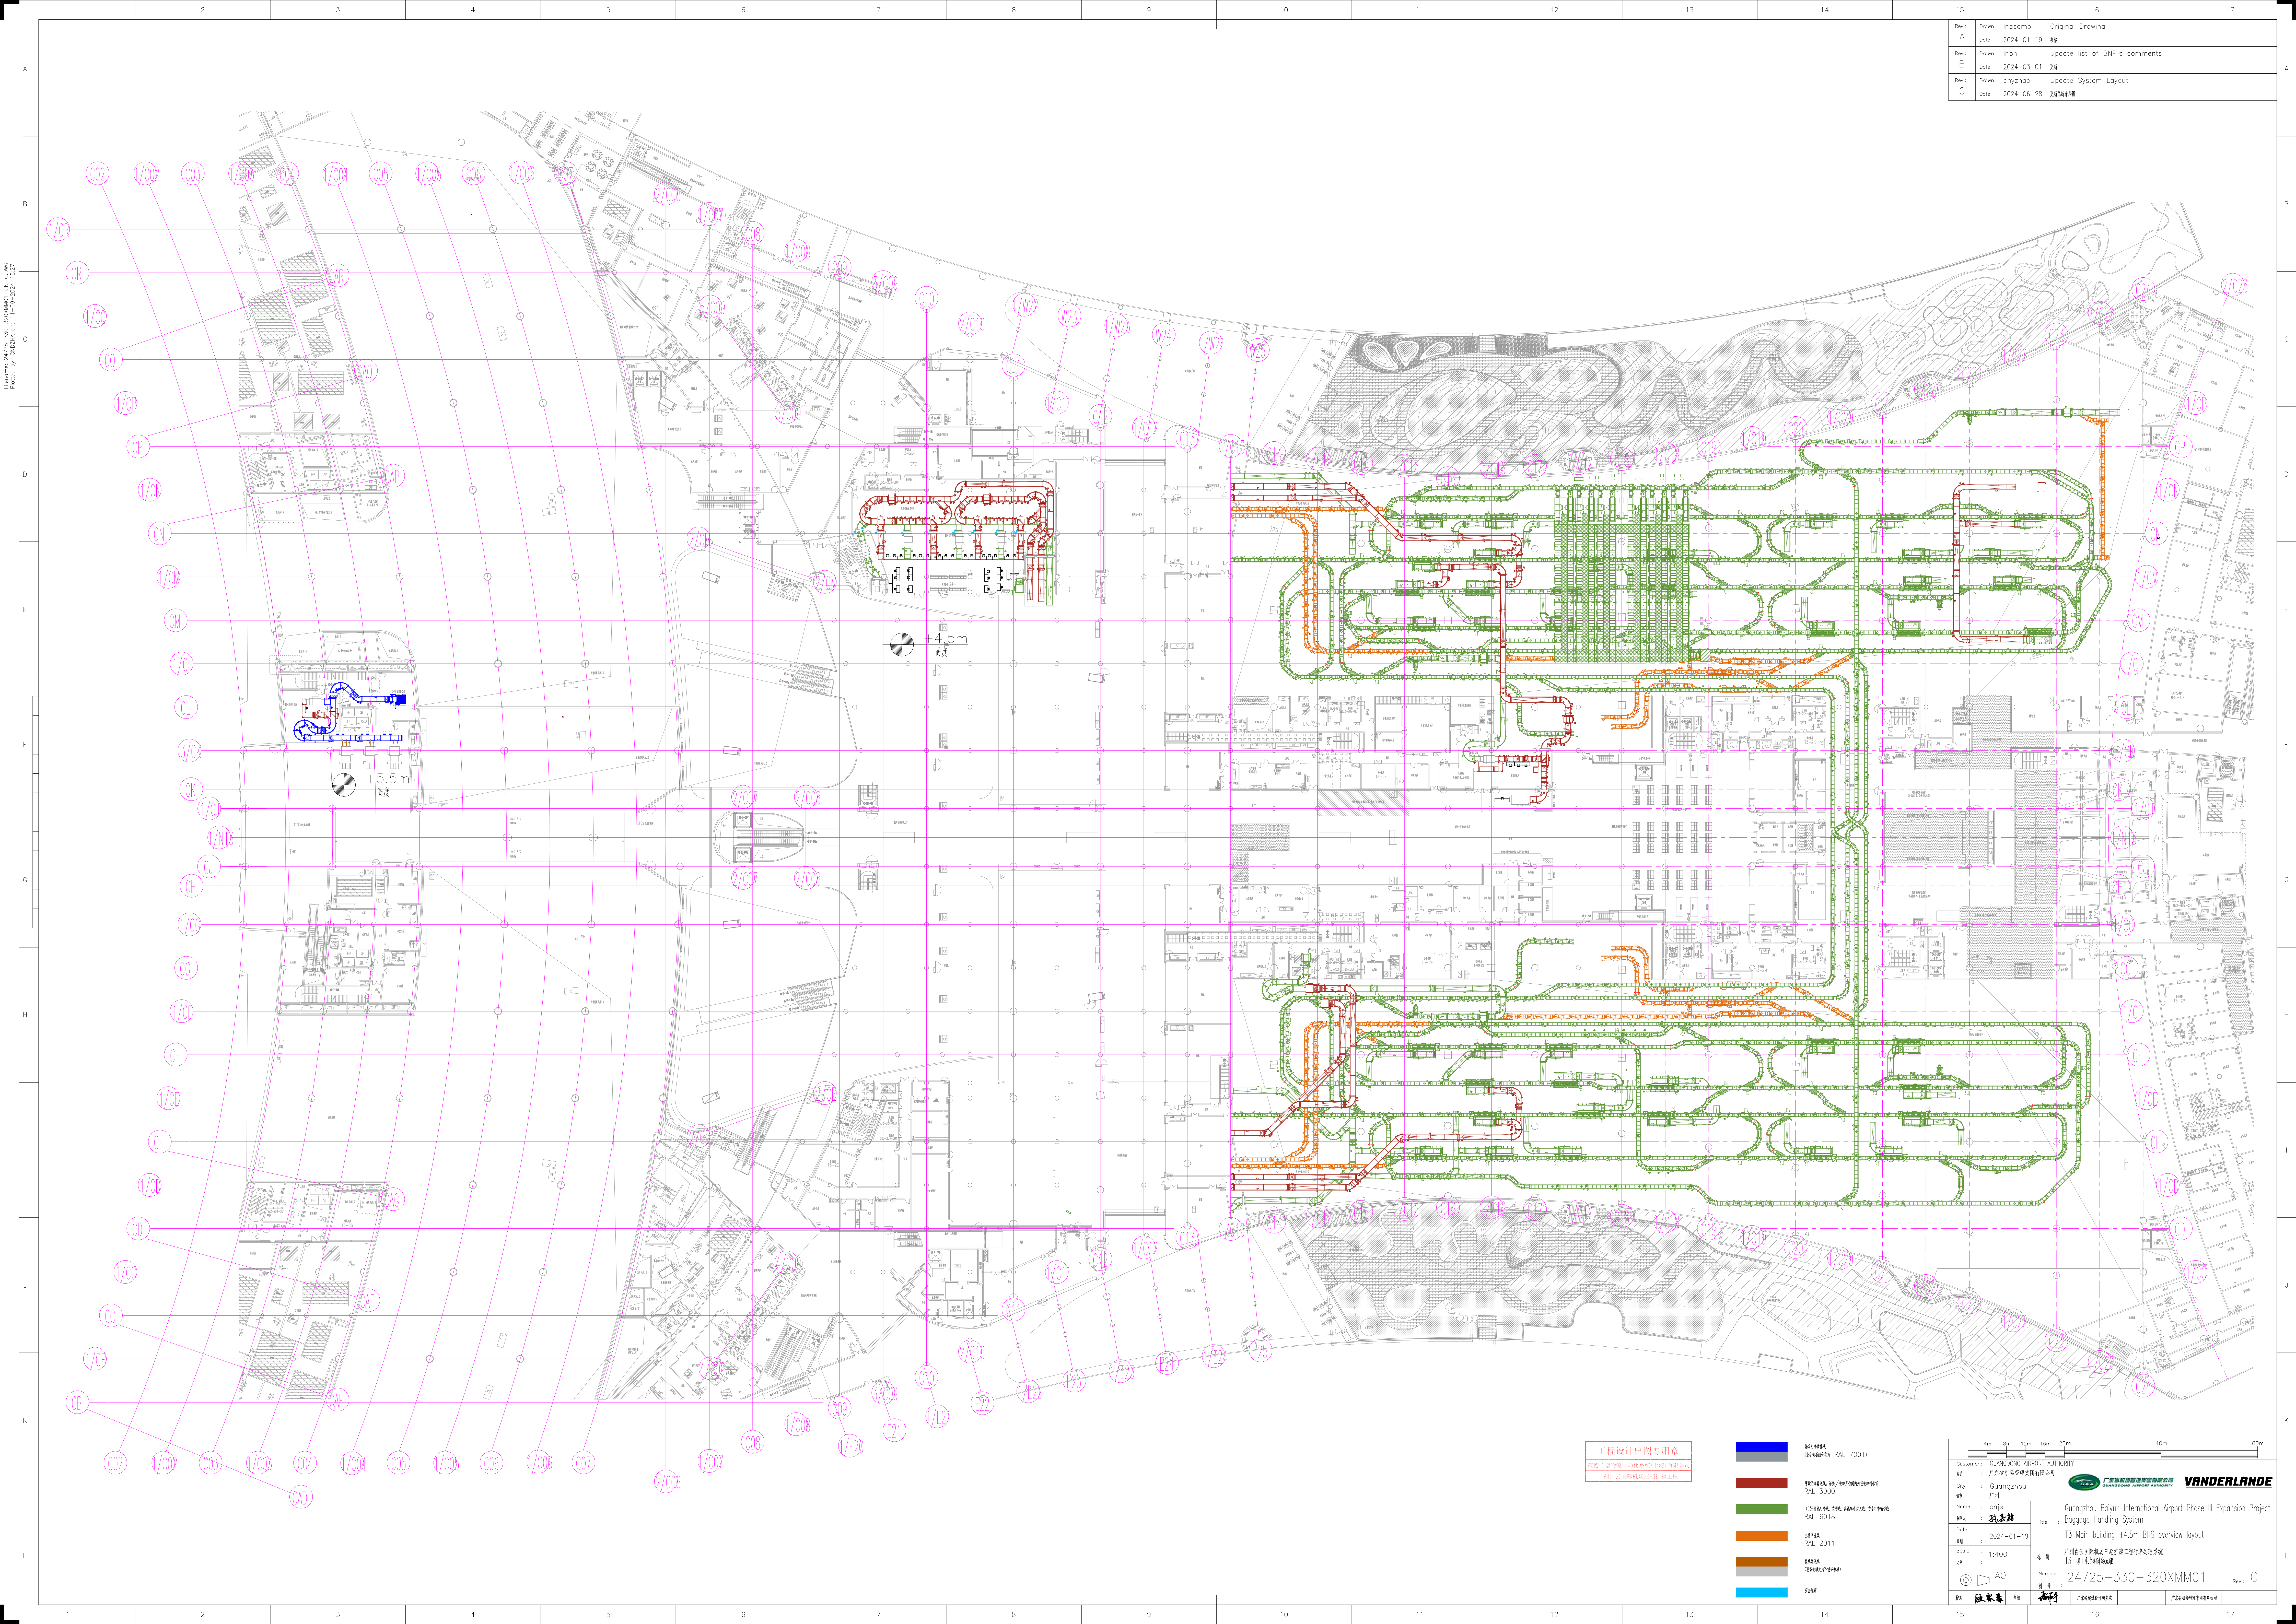

Rev:	Draw:	Inasamb	Original Drawing
A	date:	2024-01-19	何
Rev:	Draw:	Inoni	Update list of BNP's comments
B	date:	2024-03-01	无
Rev:	Draw:	cnyzhao	Update System Layout
C	date:	2024-06-28	更新系统图

工程设计出图专用章
广东省机场管理集团有限公司
广州白云国际机场航站楼三期扩建工程

- 蓝色 (RAL 7001)
- 红色 (RAL 3000)
- 绿色 (RAL 6018)
- 橙色 (RAL 2011)
- 灰色 (RAL 2011)
- 黄色 (RAL 2011)
- 白色 (RAL 2011)

Customer:	GUANGDONG AIRPORT AUTHORITY	广东机场管理集团有限公司
City:	Guangzhou	广州
Name:	cnyjs	陈永基
Date:	2024-01-19	
Scale:	1:400	
Number:	A0	
Rev:	C	
Project:	Guangzhou Baiyun International Airport Phase III Expansion Project	广州白云国际机场三期扩建工程
Title:	Baggage Handling System	行李处理系统
Content:	T3 Main building +4.5m BHS overview layout	T3主楼+4.5mBHS系统总图
Scale:	1:400	
Number:	24725-330-320XMM01	
Rev:	C	
Project:	Guangzhou Baiyun International Airport Phase III Expansion Project	广州白云国际机场三期扩建工程
Title:	Baggage Handling System	行李处理系统
Content:	T3 Main building +4.5m BHS overview layout	T3主楼+4.5mBHS系统总图
Scale:	1:400	
Number:	24725-330-320XMM01	
Rev:	C	